2025-2026

Selected Works

of Özgün Ege Bilgiç

interior design



about me

Hi, I'm Özgün!
I enjoy exploring how different spaces impact the experience and integrating these experiences back into design. I work across both physical and digital environments. I like creating stories within the interior and shaping user experience. Alongside my academic projects, I have gained experience in both interior and exterior design through my work on game projects.

education

MEF University
Bachelor of Arts in Interior Architecture
(2024-present)

İSTEK Acıbadem HS
STEM Track
(2020-2024)

languages

English (advanced)
PTE Academic Score: 69
(tinyurl.com/ozgunptescore)

Turkish (native)

work experience/ internships

DESIGN AND BUILD STUDIO INTERNSHIP
2YAKA - fada.mef.edu.tr/Portfolio/2yaka
(July-June 2025)

SITE SUPERVISION INTERN
Kointaş Gayrimenkul - Ahmet Fikret Evyap HS
(June 2026)

FREELANCE ENVIRONMENT DESIGN (NDA)
Outsource designer for unannounced game project
(January 2026 - present)

software

- PHOTOSHOP ++++
- ILLUSTRATOR ++
- INDESIGN ++
- AFFINITY +++
- AFTER EFFECTS +
- AUTOCAD ++++
- RHINOCEROS 3D ++++
- GRASSHOPPER +++
- BLENDER ++
- ENSCAPE ++++
- V-RAY +++

skills

- DIAGRAM CREATION
- 3D MODELLING
- 3D RENDERING
- 3D PRINTING
- MODEL CREATION
- VR PRESENTATION

the stage has collapsed into us! 01

we were never invited. 02

2YAKA DESIGN AND BUILD STUDIO 03

the stage has collapsed into us!


INT201

instructor: Ceren Çelik

My first project explores the concept of a theatre and redefines it by dissolving the boundary between performer and audience, turning everyone into performers for the space. Rather than designing a fixed stage, the project choreographs moments of exposure, retreat, and interaction through architecture itself.



*Daytime interior render #1

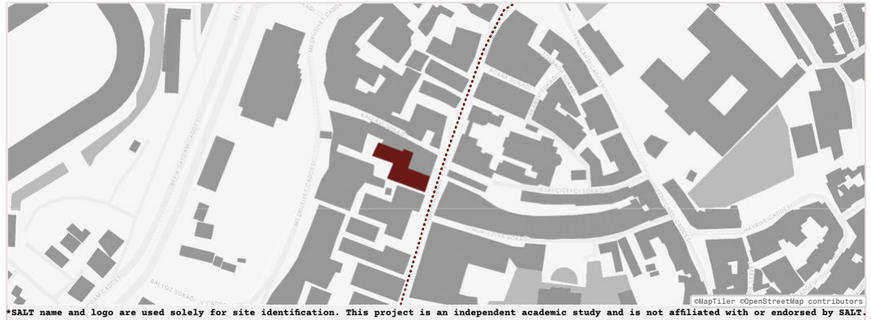

*SALT name and logo are used solely for site identification. This project is an independent academic study and is not affiliated with or endorsed by SALT.

Salt

concept and site analysis of



*Mapping of SALT Beyoğlu Building& Exhibition




*Collage about project idea

Control rarely announces itself. It emerges through repetition, expectation, and visibility, slowly becoming indistinguishable from everyday life. What begins as observation evolves into self-surveillance, where the performance of social roles no longer feels imposed, but willingly embraced as part of who we are we have become.



you are being watched you are being watched you are being watched

reading the existing stage

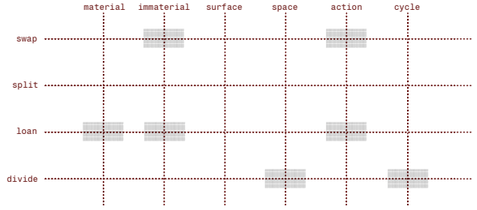

Rather than documenting buildings as isolated objects, the street was read through actions and spatial conditions. Each location paired verbs such as swap, loan, divide, and split with material, immaterial, surface, space, action, and cycle. This method revealed hidden performances embedded within everyday urban life, transforming observation into spatial strategy.


CINEMA - CYCLE DIVIDE | HIGH SCHOOL - ACTION SWAP | CATHOLIC CHURCH - IMMATERIAL SWAP

Before proposing a new stage, the existing one had to be understood. The city already performs through countless everyday encounters, where visibility, movement, and observation continuously shape public life. Istiklal Street became the place where these invisible performances could be observed and mapped.



*Collage about project idea


GRAFFITI - ACTION LOAN | TRAM - SPACE DIVIDE | POLICE - MATERIAL/ IMMATERIAL LOAN

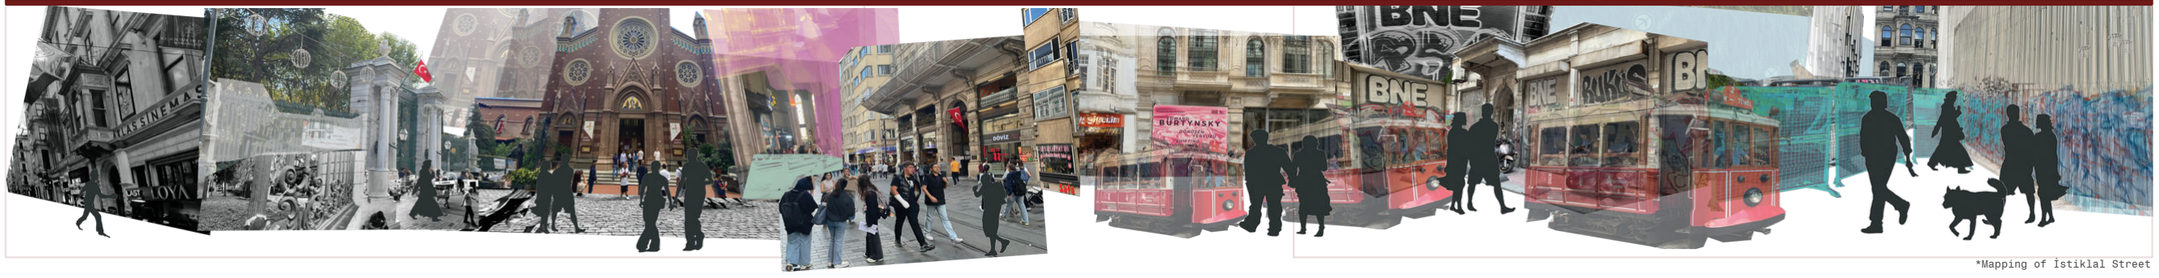


*Mapping of İstiklal Street

from privacy to performance

The project questions how surveillance becomes internalized and how individuals are gradually pushed onto a stage without consent. Through overlapping sightlines, translucent surfaces, and exposed circulation, users remain constantly aware of one another. The boundary between observer and performer dissolves, turning everyday occupation into a shared act of visibility. The space becomes both a public stage and a critical device, revealing how privacy is quietly eroded through architecture.

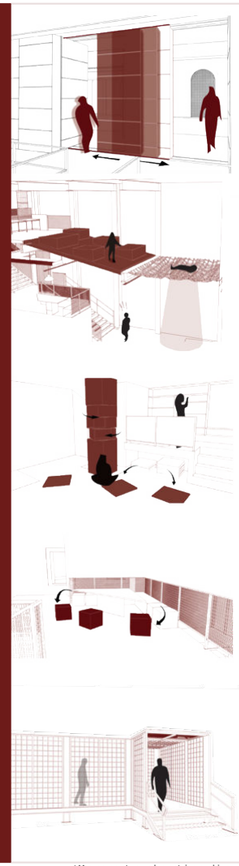

*Movement and action diagrams

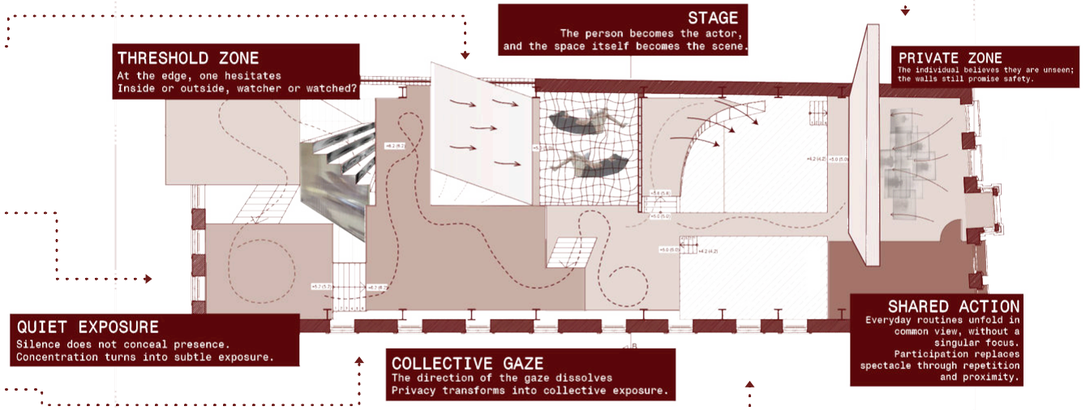

*Circulation diagram of the building



*Axonometric diagram of the building

1... Dance studio
A flexible studio for dance and focused study, allowing movement and concentration to coexist within the same space.

2... Observation tunnel
A passage that frames movement and directs attention, turning circulation into an experience of watching and being watched.

3... Presentation area
An adaptable setting for talks, screenings, and informal displays, where content and conversation can occupy the space

4... Linguistic arts room
A quiet room for reading, writing, and spoken work, supported by a semi-transparent floor.

5... Visual experience
A space for projection, viewing, and visual experimentation, where light, image, and presence are continuously emmited.


6... Main stage
Two lowered platforms form an open framework for performance, shaped by the people who occupy them.

7... Backstage
A reconfigurable support space defined by moving walls, allowing privacy, preparation, and access to shift according to use.

*Axonometric diagram of the building



*Daytime interior render #2

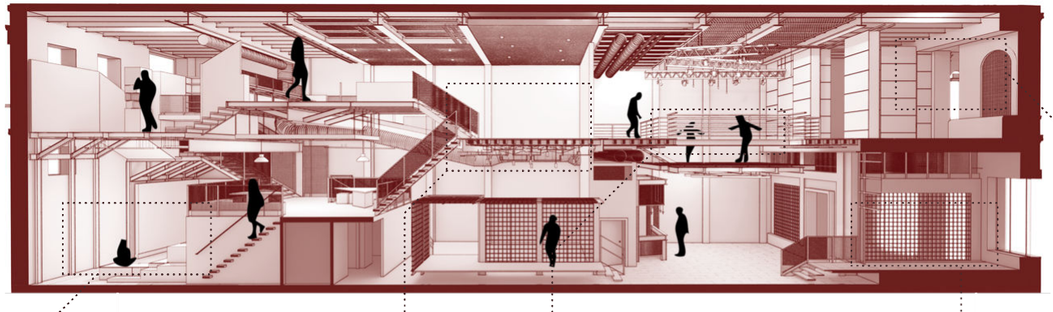

A translucent viewing surface connects both levels, allowing users to rest above while remaining partially visible from below. The area shifts between comfort, observation, and display.







Two lowered platforms form an open stage for performance, gathering, and improvised use. Positioned at the center of the project, they remain visible from multiple levels and surrounding circulation routes.



A visible studio supports dance, rehearsal, and focused study. Mirrors and adaptable surfaces turn everyday practice into a performance observed from the surrounding spaces.

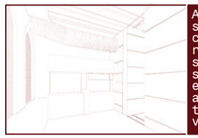

A porous threshold shifts between collective use and retreat. Movable surfaces regulate sound, privacy, and exposure while allowing preparation to remain partly visible.

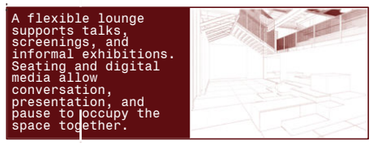

A flexible lounge supports talks, screenings, and informal exhibitions. Seating and digital media allow conversation, presentation, and pause to occupy the space together.

*Section perspective

sections

The sections reveal a spatial apparatus that erodes privacy through vertical and visual exposure. By stacking transparent and semi-open zones, the architecture turns movement into performance and everyday occupation into an act of being watched.

Surveillance emerges not as an external force, but as a condition produced by the space itself. Users move through the same architectural frame as both observers and performers, constantly negotiating visibility, retreat, and participation.

The atmosphere performs without consent, exposing the body and the gaze while turning visibility into a subtle form of control.

The atmosphere performs without consent, exposing the body and the gaze while turning visibility into a subtle form of control



*Athmosphere collage



*Daytime interior render #3




*AA Section | 1:100 Detail




*BB Section | 1:100 Detail



*CC Section | 1:100 Detail

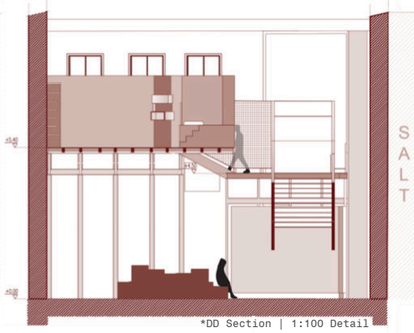

*DD Section | 1:100 Detail

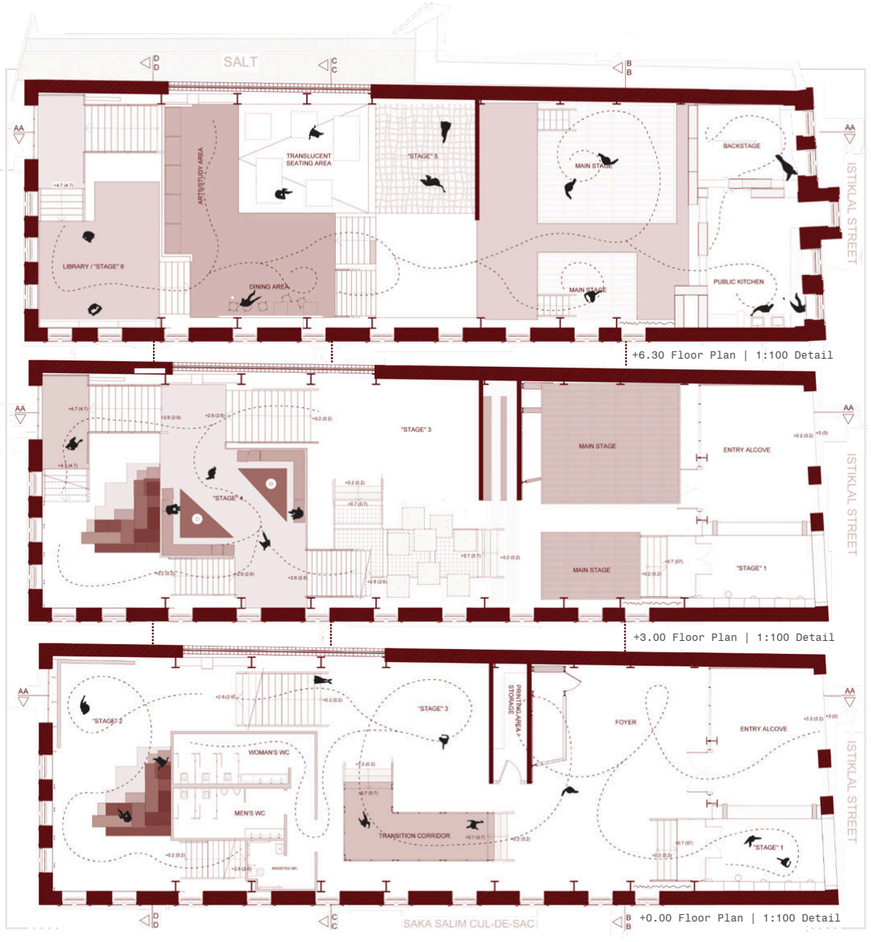




*Daytime interior render #4



*Night setting exterior render

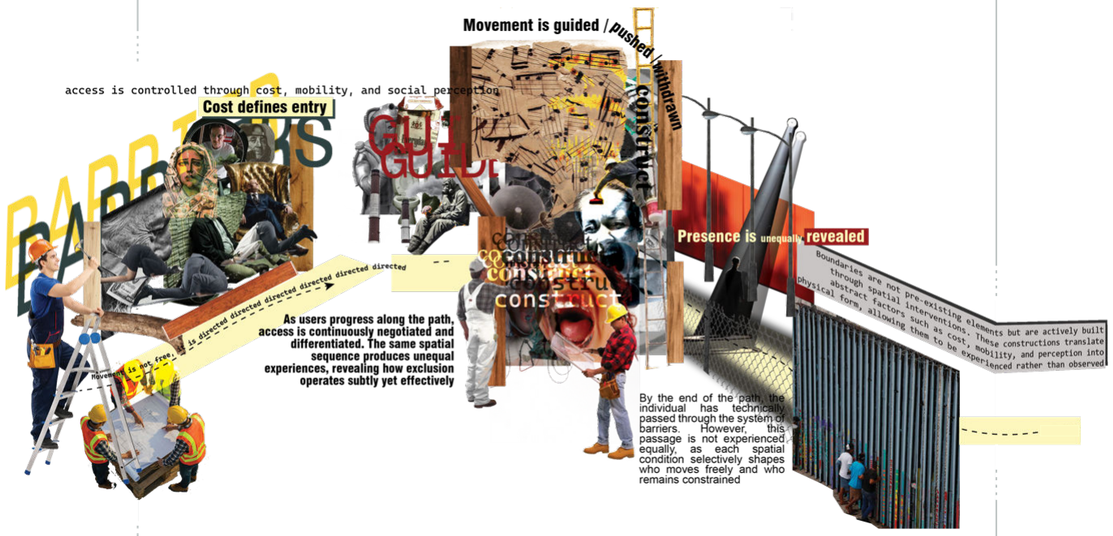


*Diagram/collage of project idea

we were never invited

INT202

instructor: Burçe Karadağ


This project begins with the invisible boundaries that shape who feels welcome, who hesitates, and who remains outside. Set within Taş Mektep, it proposes a research residence where these conditions are observed across the island, recorded, and reconstructed through small-scale spatial experiments. The building becomes a testing ground for access, belonging, and exclusion.

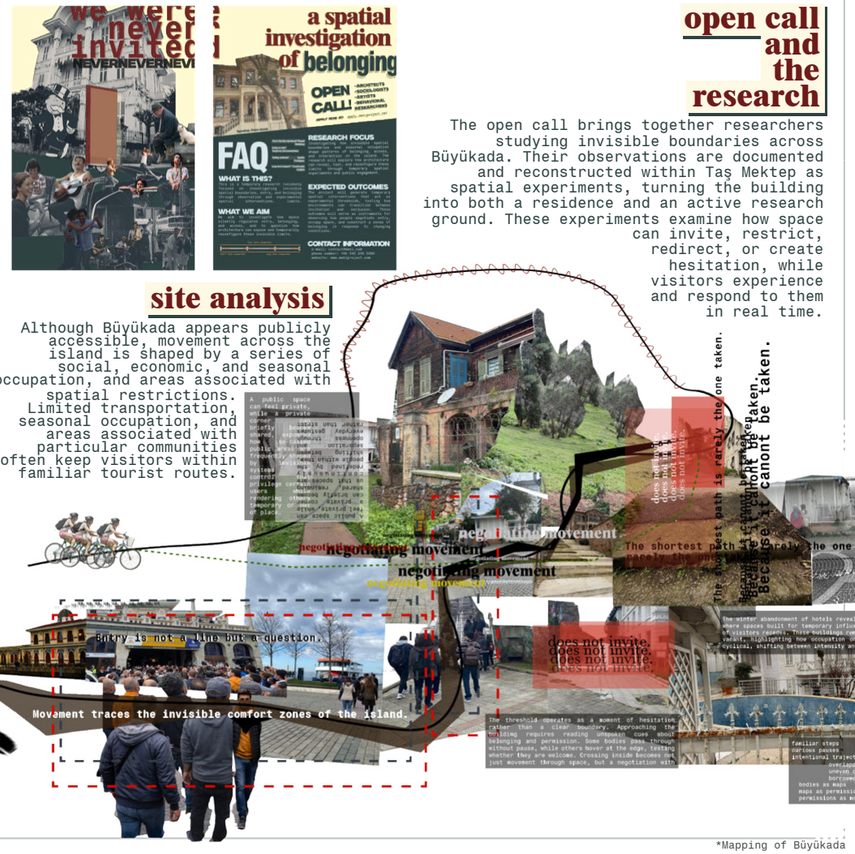


*Mapping of Büyükada



*Daytime interior render #1

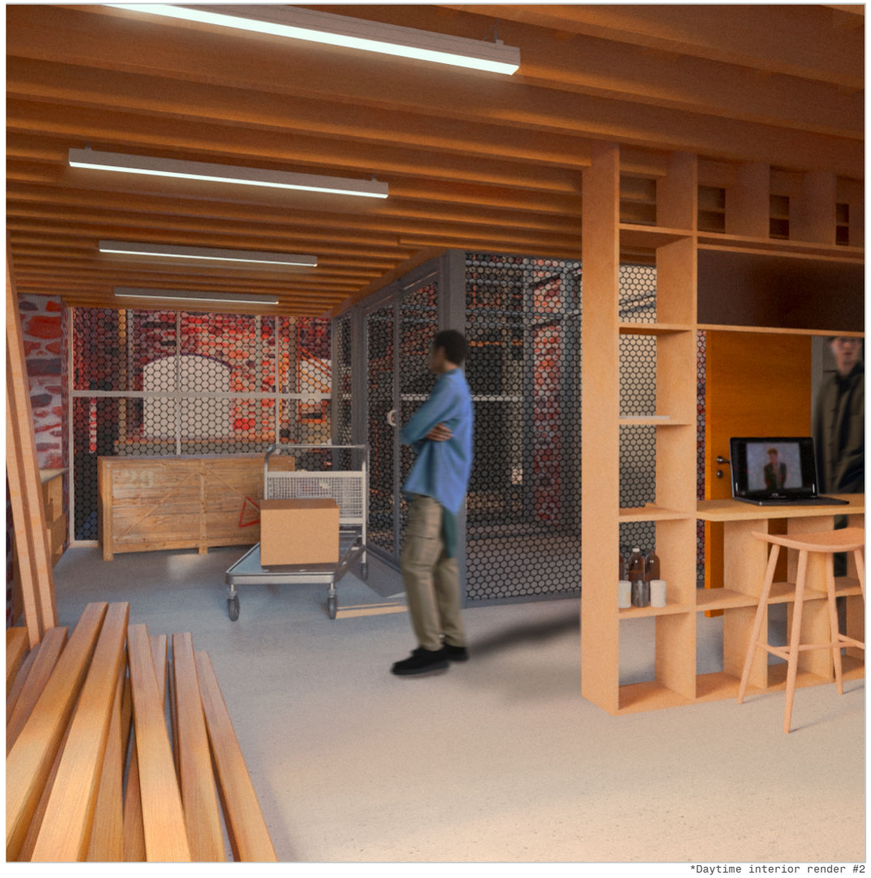

*Daytime interior render #2

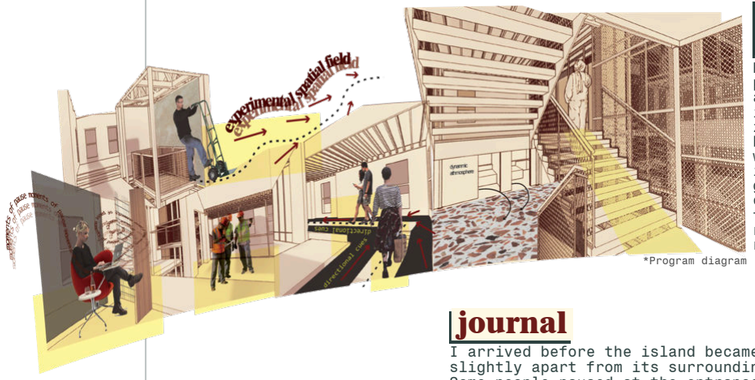

*Program diagram

program as experiment

Research, living, production, and observation are distributed across interconnected experimental zones. Each space allows boundaries to be tested, while circulation introduces moments of guidance, hesitation, and choice. The building functions not only as a residence, but as an active research instrument.


journal

I arrived before the island became crowded. Taş Mektep stood slightly apart from its surroundings, visible yet uncertain. Some people paused at the entrance, while others passed without noticing it. As the day unfolded, the threshold shifted between hesitation, brief occupation, and quiet observation. The building seemed to remain caught between invitation and distance, never fully closing itself off, yet never clearly welcoming anyone




I woke up early inside the building. Sounds from the street were already leaking in, but no one was really approaching. The building still felt slightly detached from the rhythm of the island.

*Mapping of Taş Mektep building/ journal

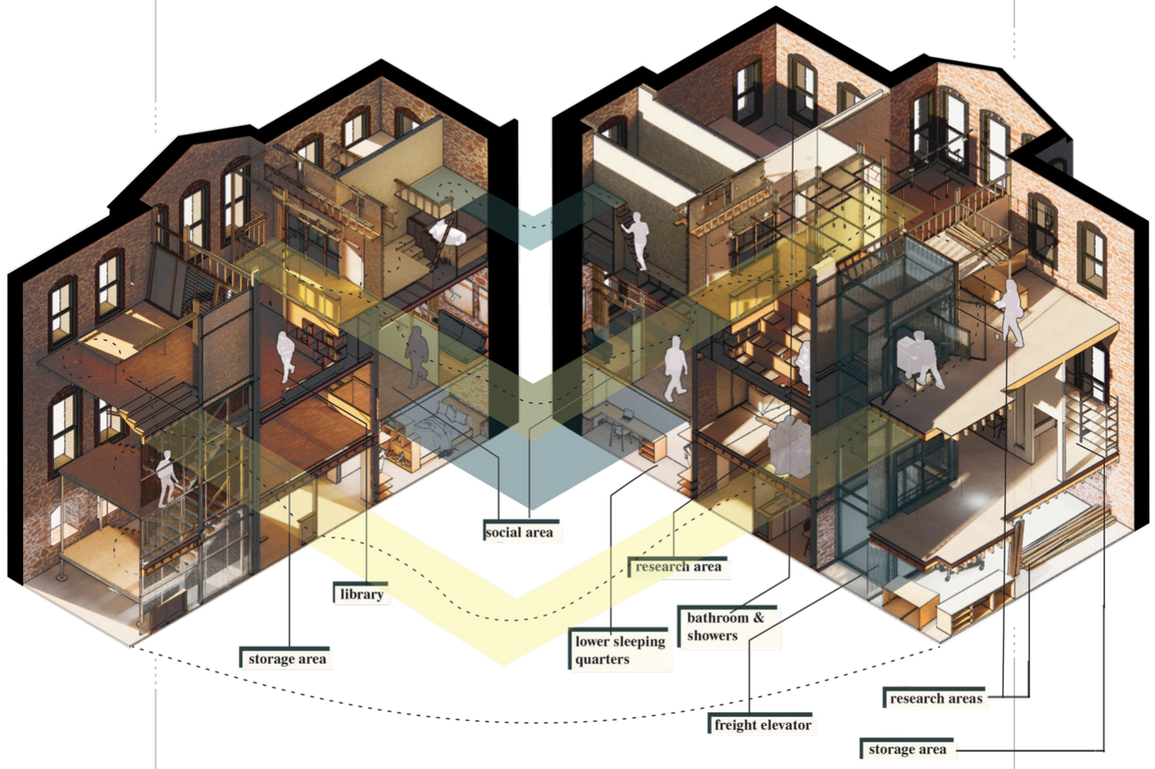

*Axonometric rotation diagram

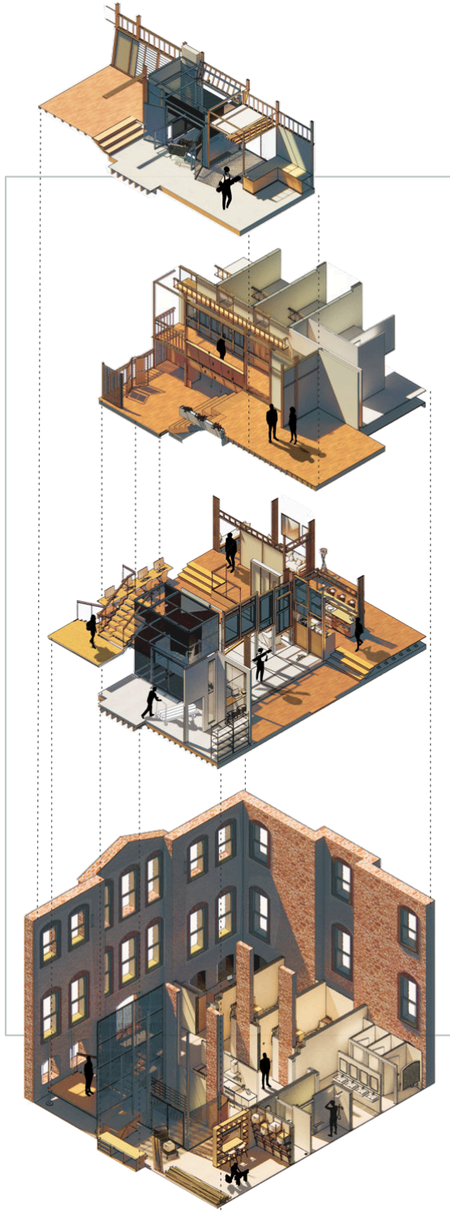


manifesto

Exclusion rarely appears as a closed door. It is embedded in everyday environments through subtle cues that shape who feels welcome, who hesitates, and who withdraws. Even spaces described as public may operate through unspoken hierarchies of familiarity, visibility, access, and perceived legitimacy.

Within Taş Mektep, these invisible conditions are reconstructed as spatial experiments. By inviting, redirecting, restricting, or suspending movement, the building becomes an active instrument for observing how architecture produces behaviour and belonging.

*Exploded axonometric

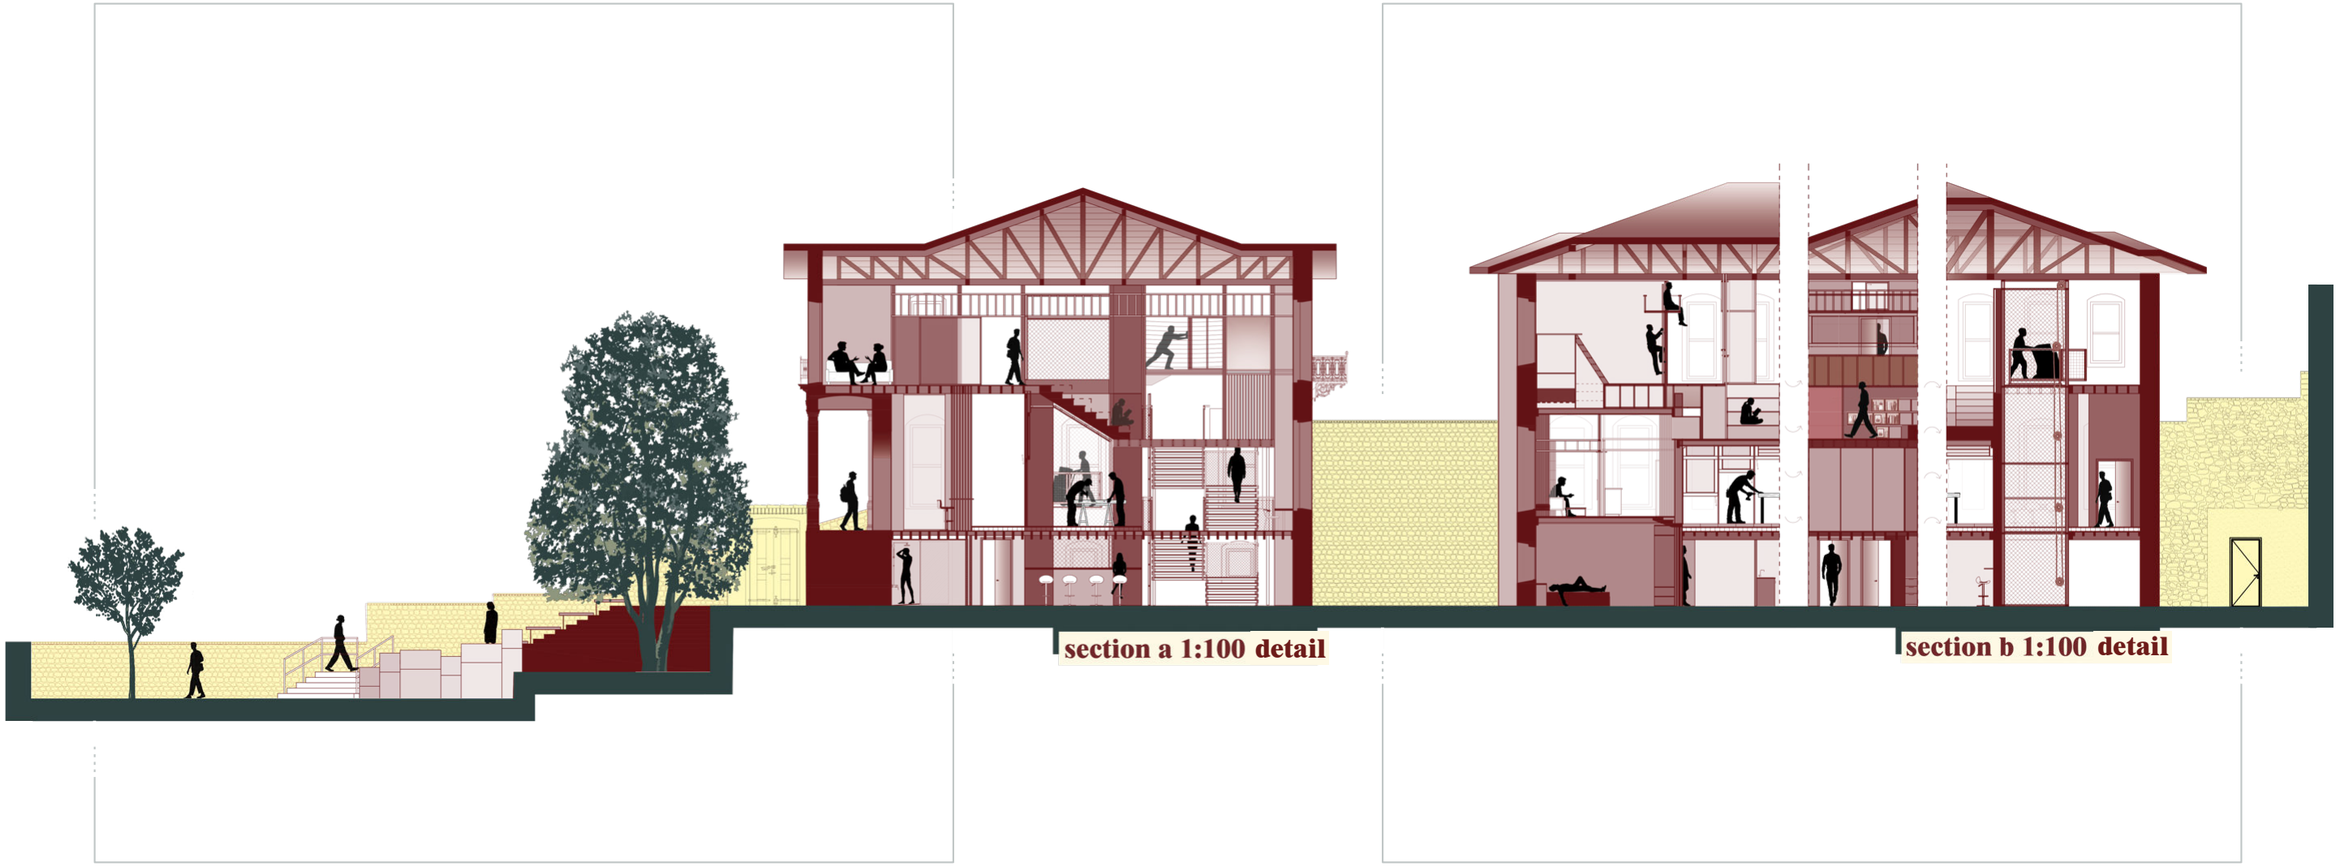

section a 1:100 detail


section b 1:100 detail


research in residence

The building distributes research, living, and production across interconnected levels. Six sleeping areas, two smaller kitchens, one shared main kitchen, a library, and common spaces support everyday life and collective exchange.

Three material workshops are linked by a large freight elevator, allowing equipment and prototypes to move vertically while keeping production connected to the shared living environment.




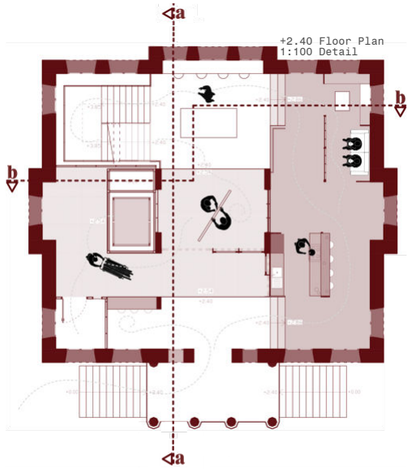

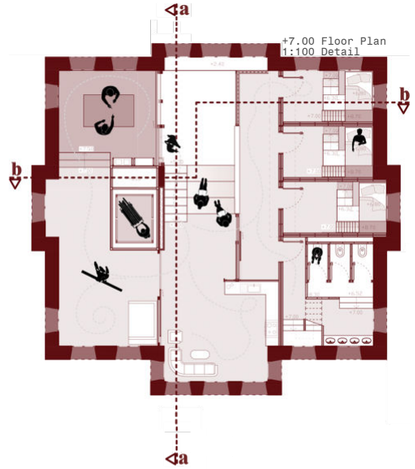



*Daytime interior render #3

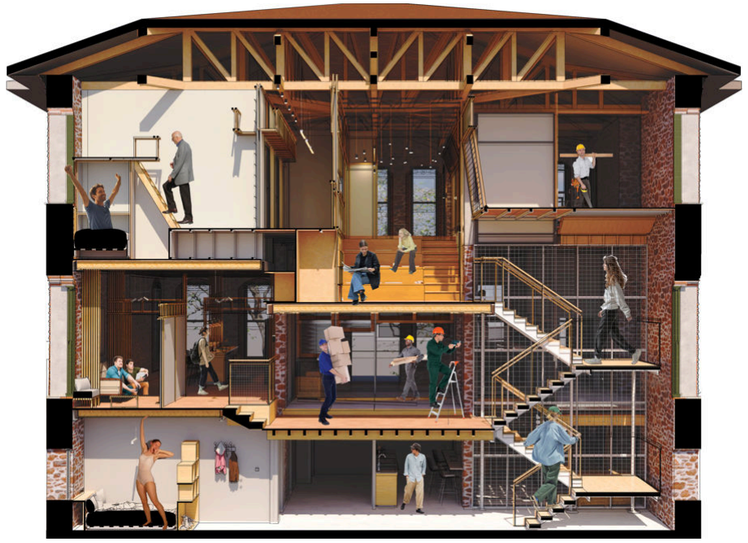

*Section perspective

testing ground

The residence provides an adaptable spatial framework where researchers can construct, modify, and test invisible boundaries. Movable elements, layered thresholds, and open structural systems allow each intervention to invite, redirect, restrict, or create hesitation. As visitors move through these changing configurations, their responses become part of the research, turning the building into a continuously evolving field of spatial experimentation.



*Athmosphere collage



*Daytime interior render #4

living the experiment

The residence is never experienced in a fixed state. As researchers construct, adjust, and remove spatial interventions, everyday routines become part of an ongoing experiment. Living, working, and observing overlap, allowing the building to change through occupation while continuously testing how space shapes movement, comfort, and belonging.



*Night setting exterior render #1

2YAKA

DESIGN AND BUILD! STUDIO

FADA 100

instructors: Derya Uzal
Hasan Murad Adalı

assistants: Çiğdem Dağdelen
Şevval Naz Yılmazer


*in collaboration with Üsküdar Municipality Parks and Gardens Directorate

contributions: concept development, design, fabrication and assembly

This project reactivates the underused seating elements of Şenol Güneş Park through a series of site-specific additions. Rather than replacing what already exists, it adapts these structures to the everyday needs of park users. Developed in collaboration with Üsküdar Municipality, the project creates new points of rest, use, and encounter.




*On-site view #1

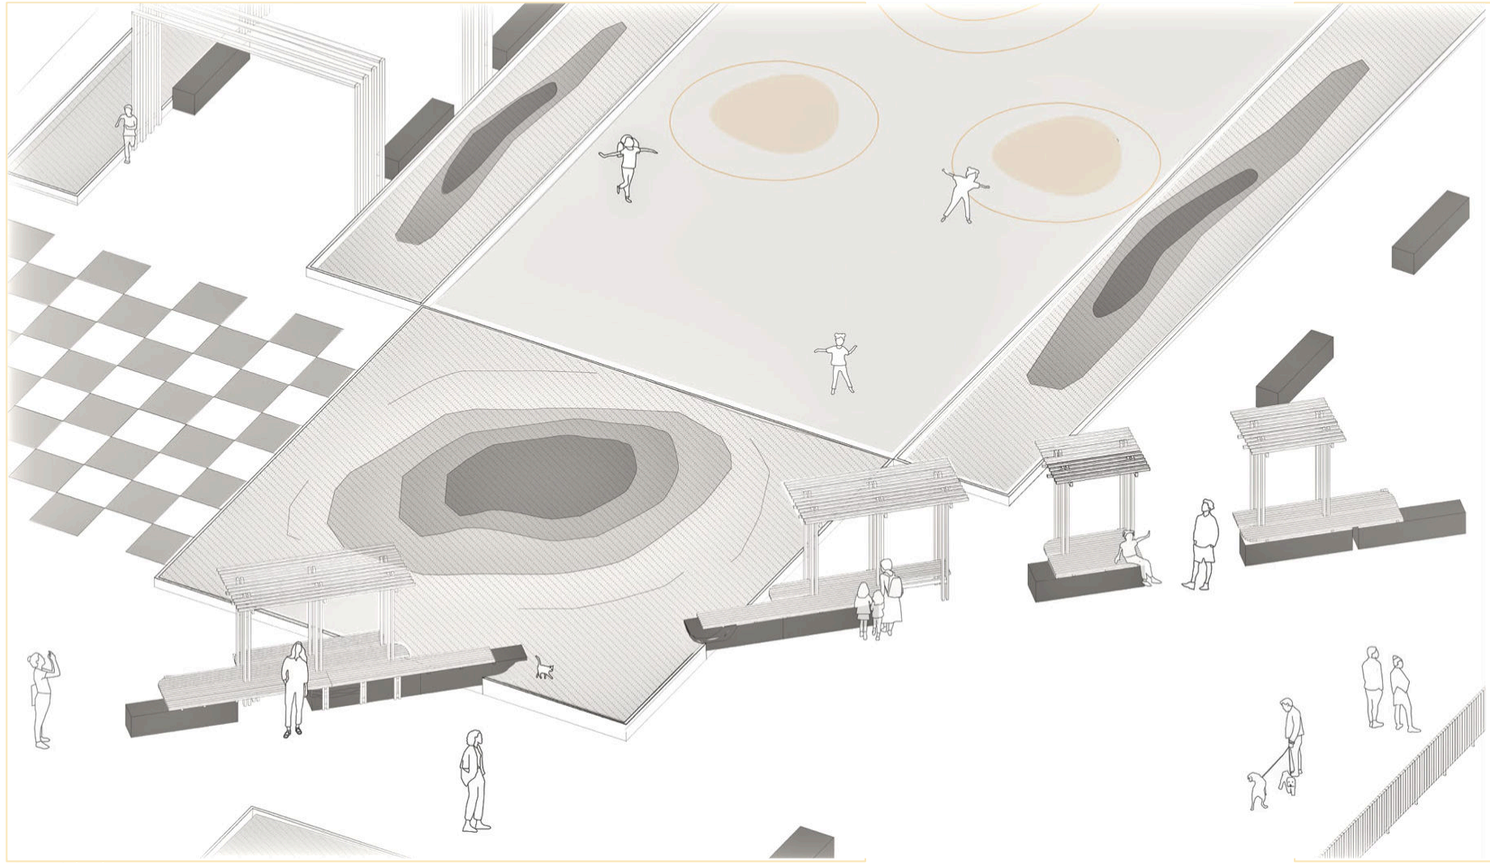

*Axonometric view


across the park

Positioned along the park’s existing seating line, the modules respond to changes in circulation, orientation, and use. Their timber frames provide shade and orient new places to sit toward the surrounding view, accommodating both individual rest and collective use. Together, the interventions form a sequence of occupied edges while keeping the central activity areas open.

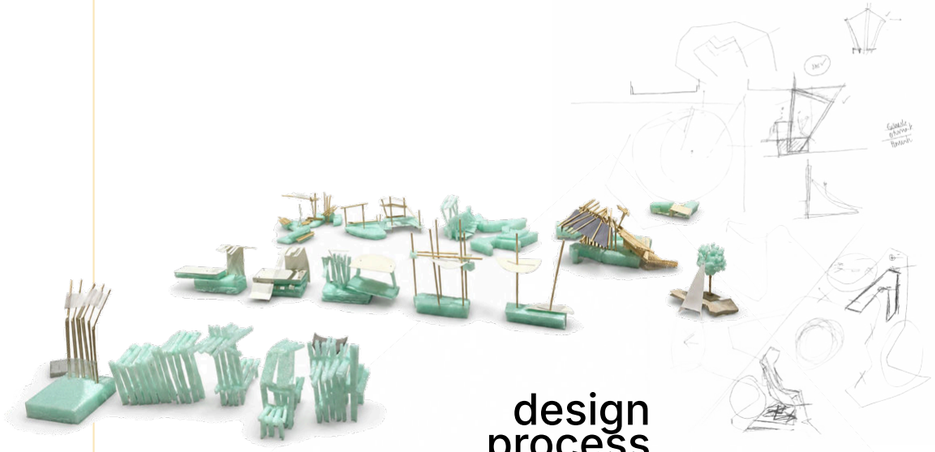



design process

The process began with quick sketches exploring different ways of extending the existing benches. These ideas were then translated into physical models, allowing variations in posture, shade, structure, and gathering to be tested together. The strongest qualities of these studies were eventually combined and developed into the final family of modules.

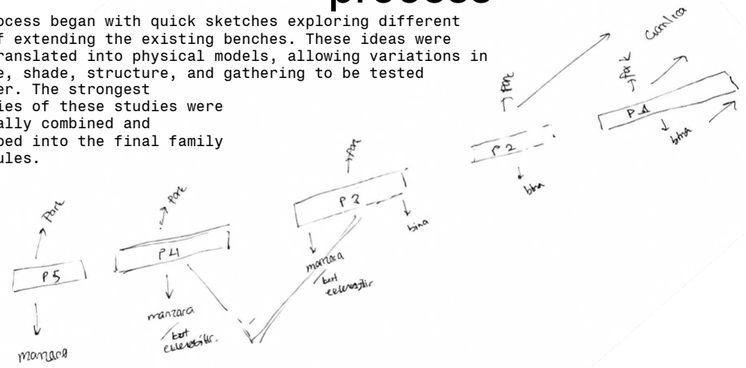


*Physical models and sketches

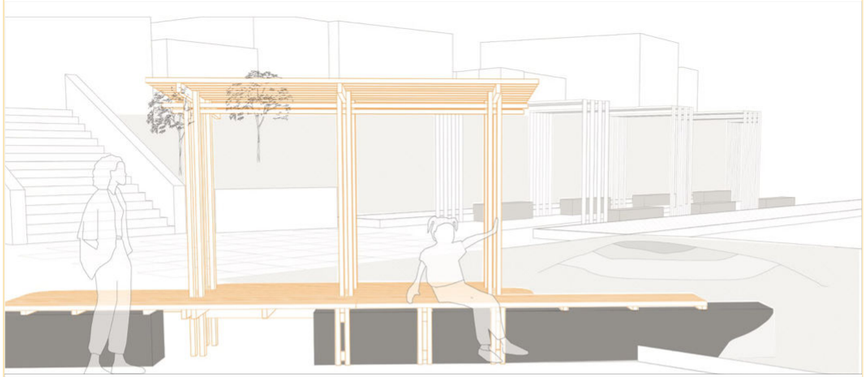

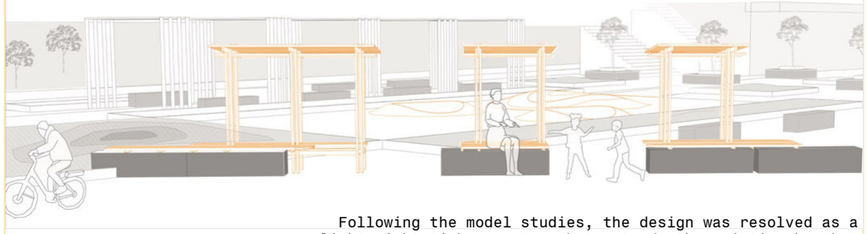


Following the model studies, the design was resolved as a lightweight timber system that extends the existing benches horizontally and introduces a canopy above. Repeated slats create shade without enclosing the park, while the open frames support different ways of sitting, leaning, and gathering. The system changes in length and orientation between locations, adapting to each bench and its view.


*Perspective view

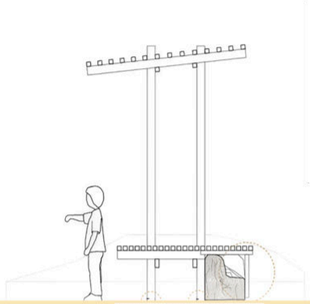


2YAKA Module #1 Section

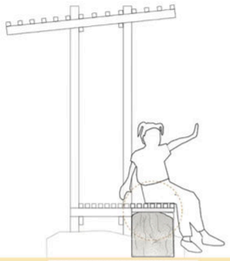

2YAKA Module #2 Section

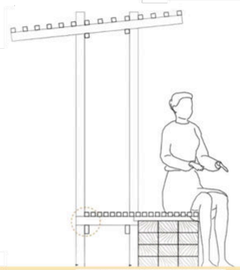


2YAKA Module #3 Section

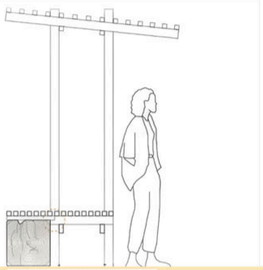

2YAKA Module #4 Section




2YAKA Module #1 Plan

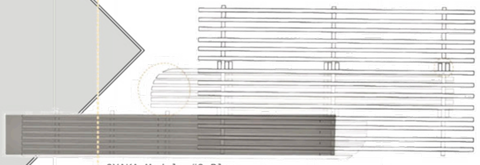


2YAKA Module #2 Plan



2YAKA Module #3 Plan

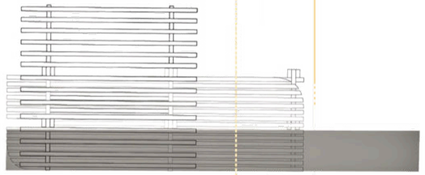

2YAKA Module #4 Plan

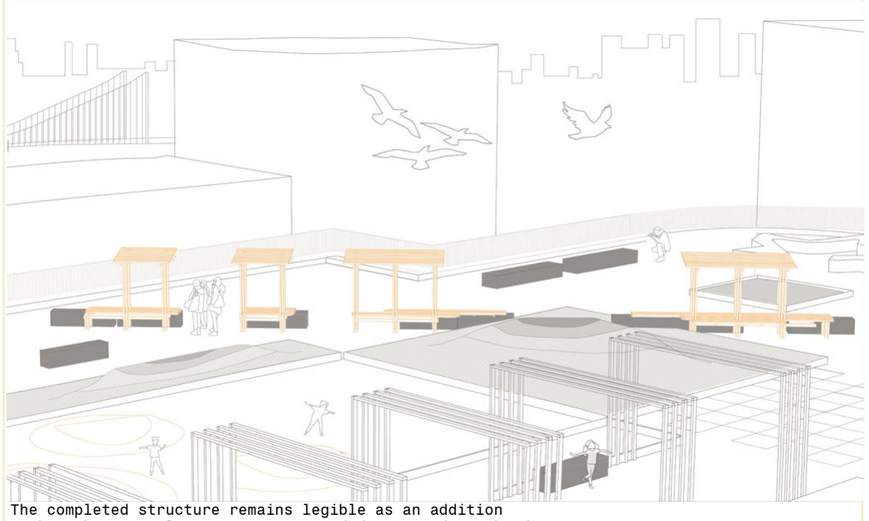

The completed structure remains legible as an addition rather than a replacement. Its extended seat and overhead frame accommodate sitting, gathering, and informal play while keeping the original bench in use.

*Site perspective



*On-site view #2



*On-site view #3



*On-site view #4



*On-site view #5



*On-site view #6


GALBA RESTAURANT
ÜSKÜDAR
BOĞAZİÇİ

Thank you!

contact: bilgicoz@mef.edu.tr | +90 545 236 5089